



COPACHISA
Quality to build prestige;
Excellence to yield outcomes.
Valle Escondido 5700 Col. Valle del Ángel
Chihuahua México. 31125 Tel: (52) 614 439.3900
www.copachisa.com

General Notes:
1. CONSULTAR LOS PLANOS DE PROPIEDAD DE COPACHISA S.A. DE C.V. CUANDO SEAN NECESARIOS PARA DETERMINAR EL PERÍMETRO DE LOS CONDOMINIOS Y LOS LÍMITES DE LOS CONDOMINIOS Y LOS LÍMITES DE LOS CONDOMINIOS.
2. EL CONDOMINIO DE LOS CONDOMINIOS Y PROPIEDAD DE COPACHISA S.A. DE C.V. ES UN CONDOMINIO PROHIBIDO TOCAR O MODIFICAR SIN EL CONSENTIMIENTO DE LA COMISIÓN DE CONDOMINIOS.

Etapa de Proyecto / Project Stage:

CONSTRUCTION

Sellos / Stamps:

REVISADO POR: M.R.A.

FECHA: 04 DE NOVIEMBRE DEL 2024

APROBADO POR:

Nombre Proyecto / Project Name:



AI
American Industries
AIG CUU INV III TRISTONE TIS
PARQUE INDUSTRIAL SUR
CHIHUAHUA, CHIH.

Aprobación por el Cliente / Client Approval:

Nombre / Name: _____

Fecha / Date: _____

Firma / Signature: _____

Escala / Scale: 1:400

Líder de Diseño / Lead Designer: ARO ANAHISA JUAREZ

Coordinador de Diseño / Design Coordinator: ARO MARTIN ROBLES

Dibujó / Drawn by: ARO JORGE LUJAN

Perito Constructor / Registered Engineer: _____

Consultores / Consultants:

Modificaciones / Changes:

Rev. # Descripción
1. SE ELIMINA MURO DE BLOQUE EN BAÑOS Y SU RESPECTIVO E.E. SE MUEVE MODELO DE BAÑO COMPLETO 3 CM HACIA EL EJE 3

Número de Proyecto / Project Number: 24044

Fecha de Elaboración / Elaboration Date: 04 DE NOVIEMBRE DEL 2024

Título del Plano / Drawing Title:


SIMBOLOGIA DE PUERTAS
DOORS LEGEND

Número de Plano / Drawing Number: A700

Número Revisión / Revision Number: 1

SIMBOLOGIA / LEGEND	
NOMBRE Y NÚMERO DE ESPACIO / SPACE NAME AND NUMBER	
NIVEL DE PISO TERMINADO (CON ACABADO) / FLOOR FINISH LEVEL (WITH FINISH)	
SÍMBOLO IDENTIFICADOR DE PUERTA / DOOR TAG	

NOTAS GENERALES / GENERAL NOTES	
A100	SERIE PLANTA DE CONSULTA / SITE PLAN SERIES
A200	SERIE PLANTAS ARQUITECTONICAS / FLOOR PLANS OR PARTIAL FLOOR PLANS SERIES
A300	SERIE TIPOS DE MUROS / WALL TYPES SERIES
A710	SERIE CEDULA DE PUERTAS / DOOR SCHEDULE SERIES
A720	SERIE CEDULA DE VENTANAS / WINDOW SCHEDULE SERIES
N.P.T. 426.00 = 0.00 P.F.L. 426.00 = 0.00	

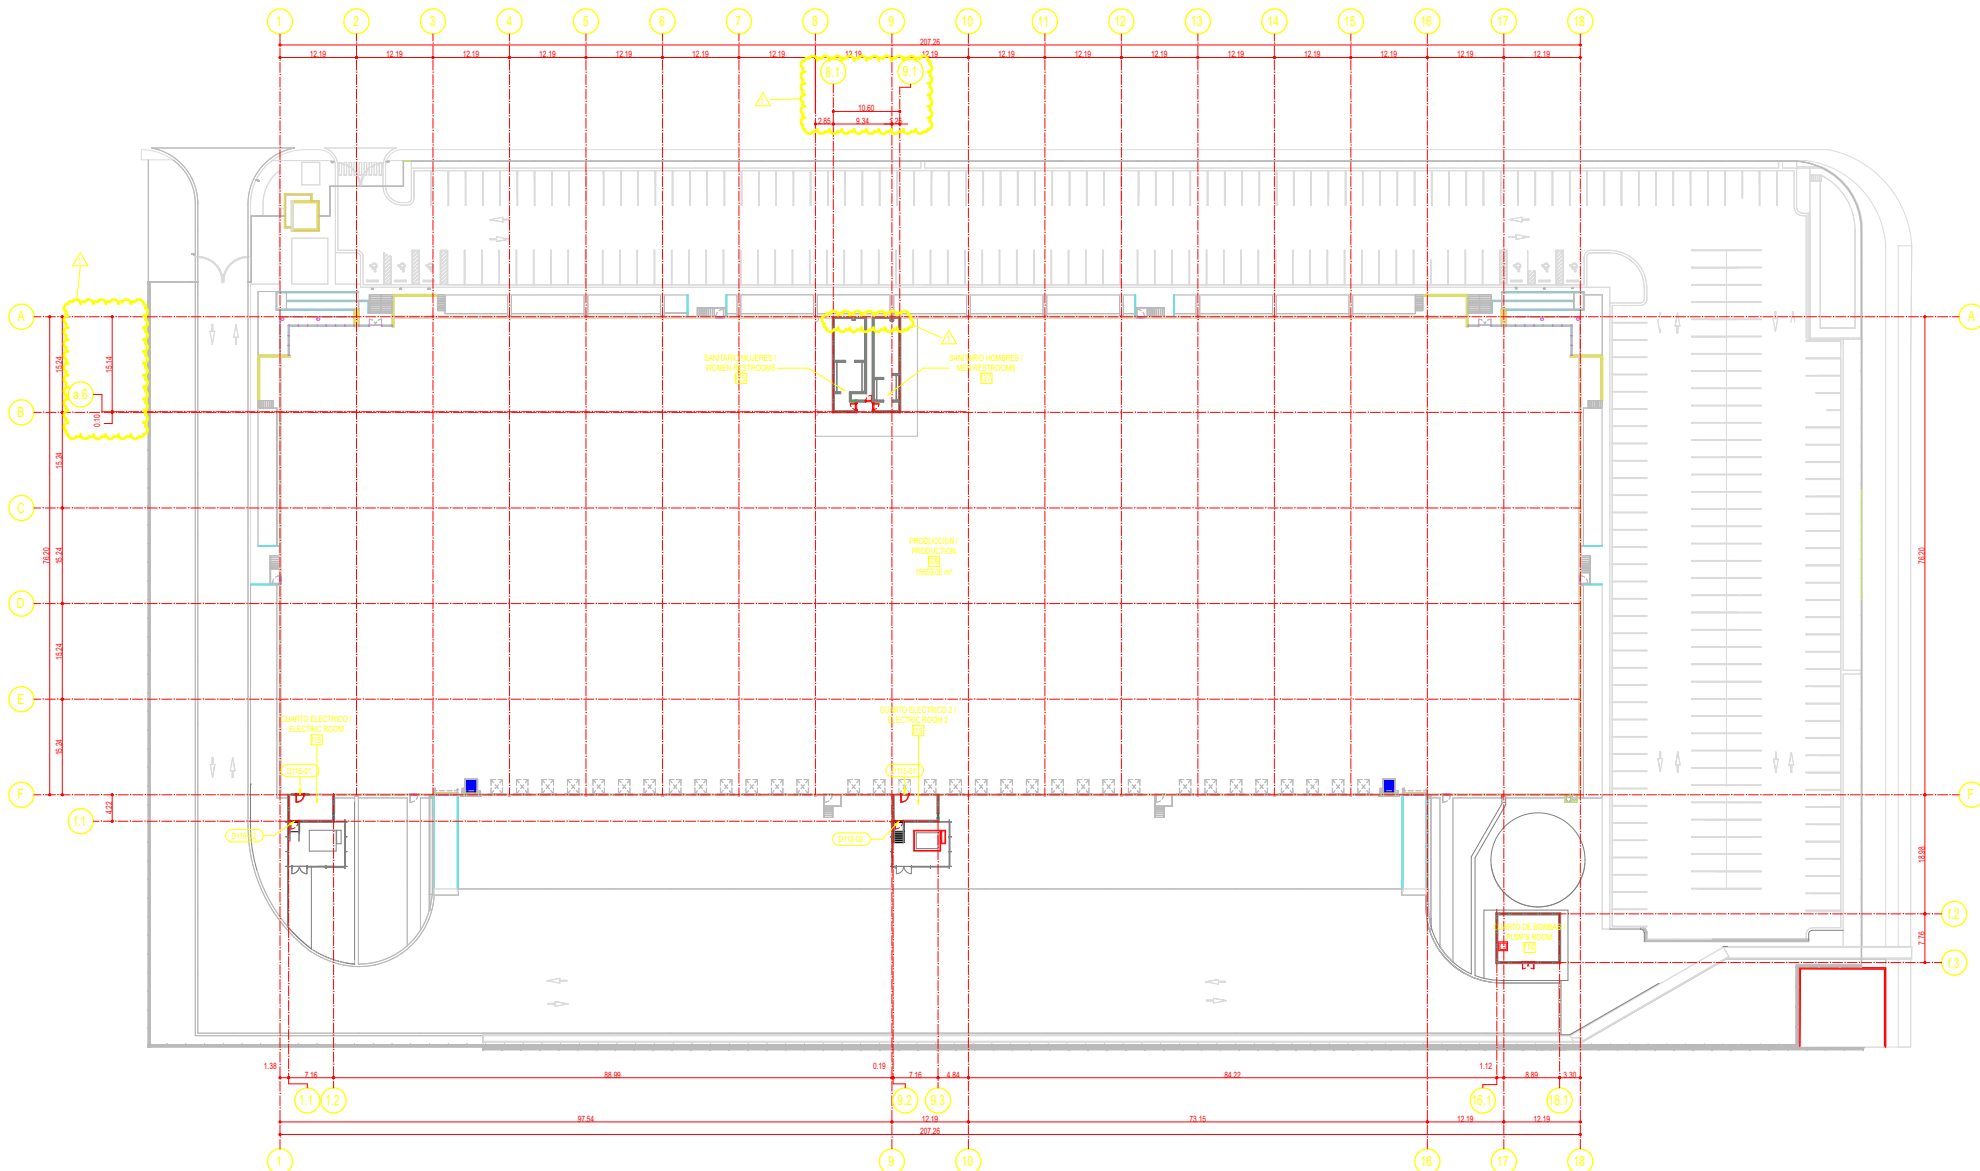

TRUE NORTH



PLANTA ARQUITECTONICA /
GENERAL ARCHITECTURAL PLAN

A1
A700

1:400