


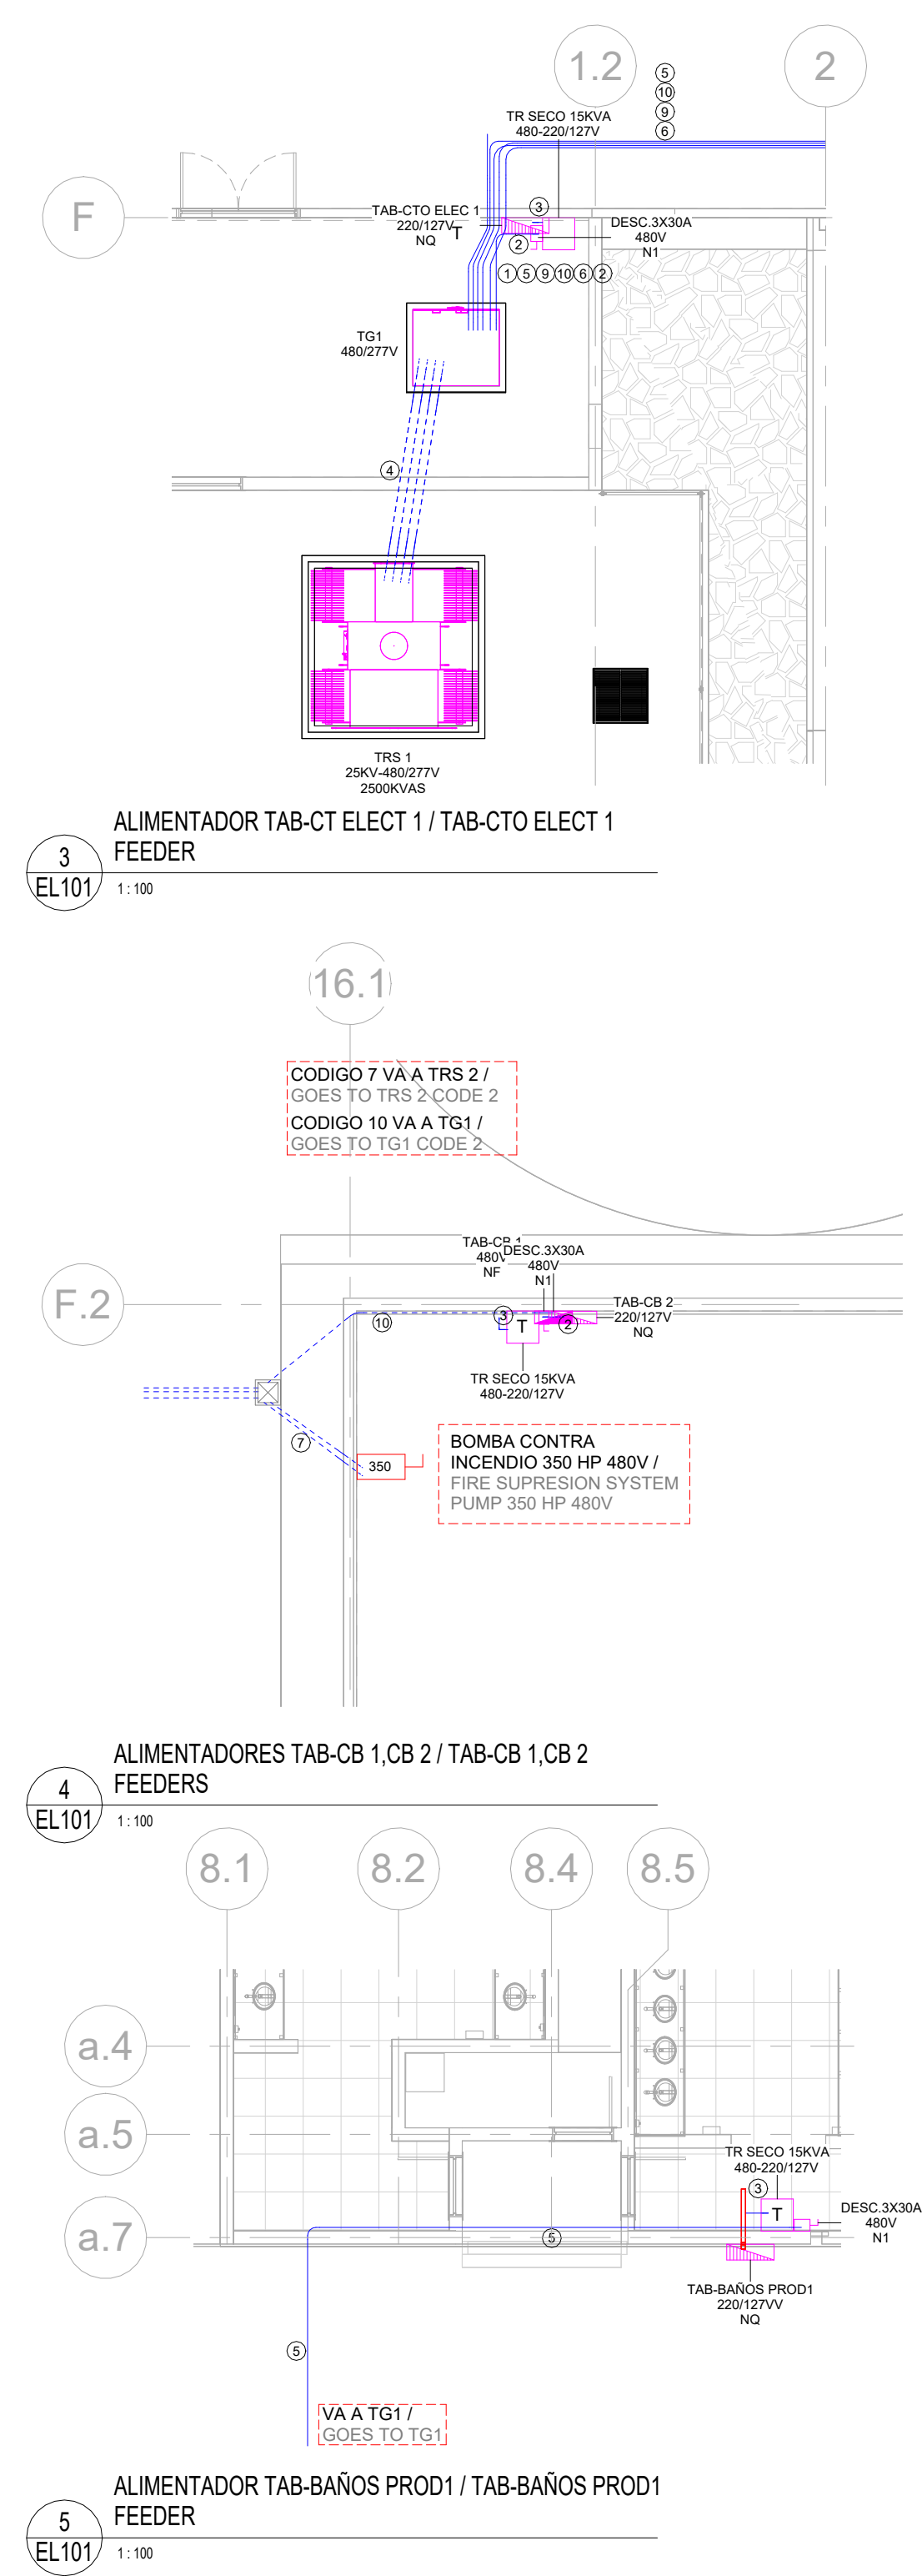

CÓDIGO DE CABLEADO / WIRING CODE					
①	3-6 AWG (F) 1-6 AWG (N) 1-10D AWG (T) 1T-41mm	②	3-10 AWG (F) 1-12D AWG (T) 1T-16mm	③	3-8 AWG (F) 1-8 AWG (N) 1-10D AWG (T) 1T-21mm
				④	24-500 AWG (F) 8-500 AWG (N) 16-30D AWG (T) 8T-101mm
⑤	3-6 AWG (F) 1-6 AWG (N) 1-10D AWG (T) 1T-27mm	⑦	6-250 AWG (F) 2-30D AWG (T) 2T-63mm	⑧	6-250 AWG (F) 1-30D AWG (T) 1CH-9"
				③	3-4 AWG (F) 1-4 AWG (N) 1-8D AWG (T) 1T-35mm
				⑩	3-2 AWG (F) 1-4D AWG (T) 1T-35mm

NOMENCLATURA / NOMENCLATURE

(F)= CONDUCTOR DE FASE / PHASE CONDUCTOR
(N)= CONDUCTOR NEUTRO / NEUTRAL CONDUCTOR
(T)= CONDUCTOR DE TIERRA / GROUND CONDUCTOR
(R)=RETORNO / RETURN
T= TUBERIA CONDUIT/ CONDUIT

RESPONSABLE DEL PROYECTO

ING. JAVIER NUÑEZ MARMOLEJO
CEDULA PROFESIONAL: 5814603