



COPACHISA
Quality to build prestige;
Excellence to yield outcomes.
Valle Escondido 5700 Col. Valle del Ángel
Chihuahua México. 31125 Tel: (52) 614 439.3900
www.copachisa.com

Notas Generales:
- EL CONTENEDOR DE ESTOS PLANOS ES PROPIEDAD DE COPACHISA S.A. DE C.V. QUEDA PROHIBIDO HACER REPRODUCCIONES Y REIMPRESIONES DE LOS CONTENIDOS SIN EL CONSENTIMIENTO DE LA EMPRESA.
- LOS DISEÑOS DEBEN ENTENDERSE SOBRE EL DISEÑO.

General Notes:
- THE CONTENT OF THIS DRAWING IS PROPERTY OF COPACHISA S.A. DE C.V. IT IS EXPRESSLY PROHIBITED TO REPRODUCE OR REPRINT WITHOUT THE CONSENT OF THE COMPANY.

Etapas de Proyecto | Project Stage:

CONSTRUCTION

Sellos | Stamps:

REVISADO POR: M.R.A.

FECHA: 28 DE OCTUBRE DEL 2024

APROBADO POR:

Nombre Proyecto | Project Name:



AIIG CUU INV III TRISTONE TIS
PARQUE INDUSTRIAL SUR
CHIHUAHUA, CHIH.

Aprobación por el Cliente | Client Approval:

Nombre | Name: _____

Fecha | Date: _____

Firma | Signature: _____

Escala | Scale: 1:450

Líder de Diseño | Lead Designer: ARO. ANAHISA JUAREZ

Coordinador de Diseño | Design Coordinator: ARO. MARTIN ROBLES

Dibujó | Drawn by: ARO. JORGE LUJAN

Perito Constructor | Registered Engineer: _____

Consultores | Consultants:

Modificaciones | Changes:

Rev. # Cmo Descripción

Numero de Proyecto | Project Number: 24044

Fecha de Elaboración | Elaboration Date: 28 DE OCTUBRE DEL 2024

Título del Plano | Drawing Title:

PLANO DE ESCALERAS EXTERIORES

EXTERIOR STAIRS PLAN


Numero de Plano | Drawing Number: A250

Numero Revisión | Revision Number:

NOTAS GENERALES

- A100 SERIE PLANTA DE CONJUNTO/
SITE PLAN SERIES
A228 SERIE DETALLE DE ANDENES/
DOCKS DETAILS SERIES
A400 SERIE DE CORTES/
SECTION SERIES
A500 SERIE TIPOS DE MURO/
WALL TYPES SERIES
A600 SERIE FACHADAS/
ELEVATIONS SERIES
A700 SERIE CENALA DE PUERTAS Y VENTANAS/
DOORS AND WINDOWS SCHEDULES SERIES

EL N.P.T. 1,359.95 ± 0.00
THE F.F.L. 1,359.95 ± 0.00

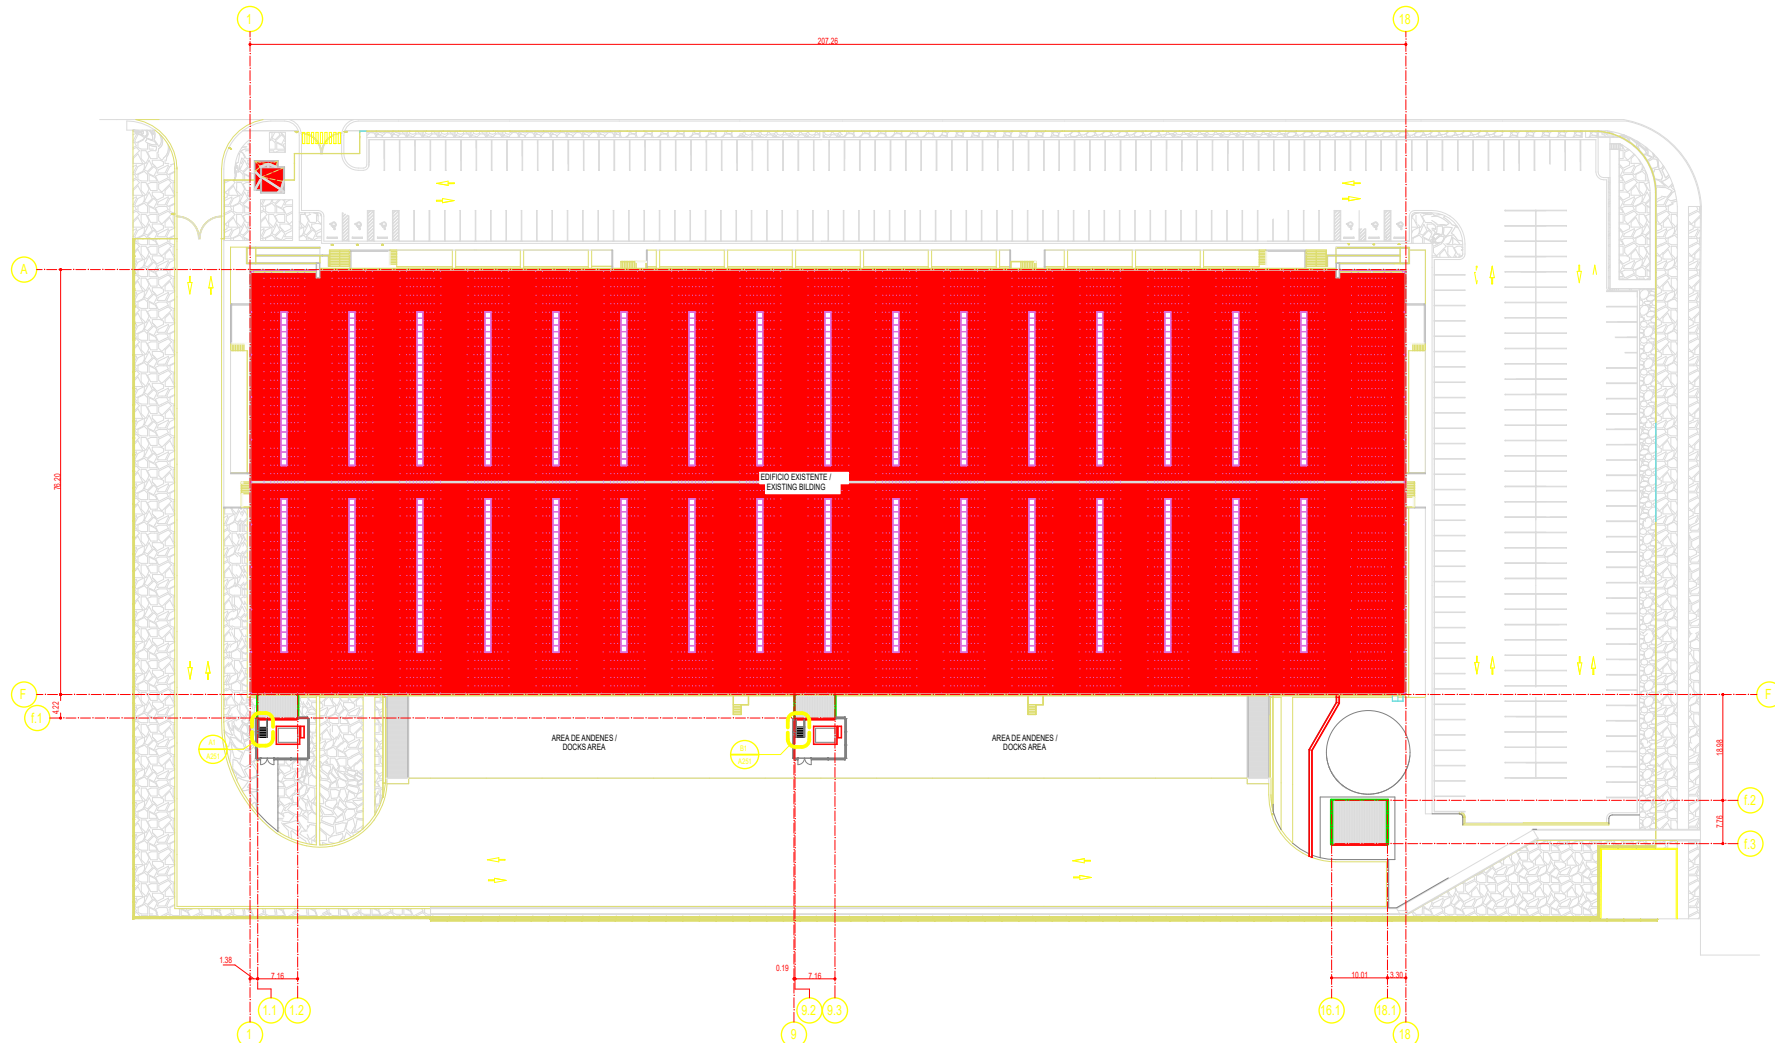

PLANTA DE CONJUNTO /

SITE PLAN

A1

A250

1:450